


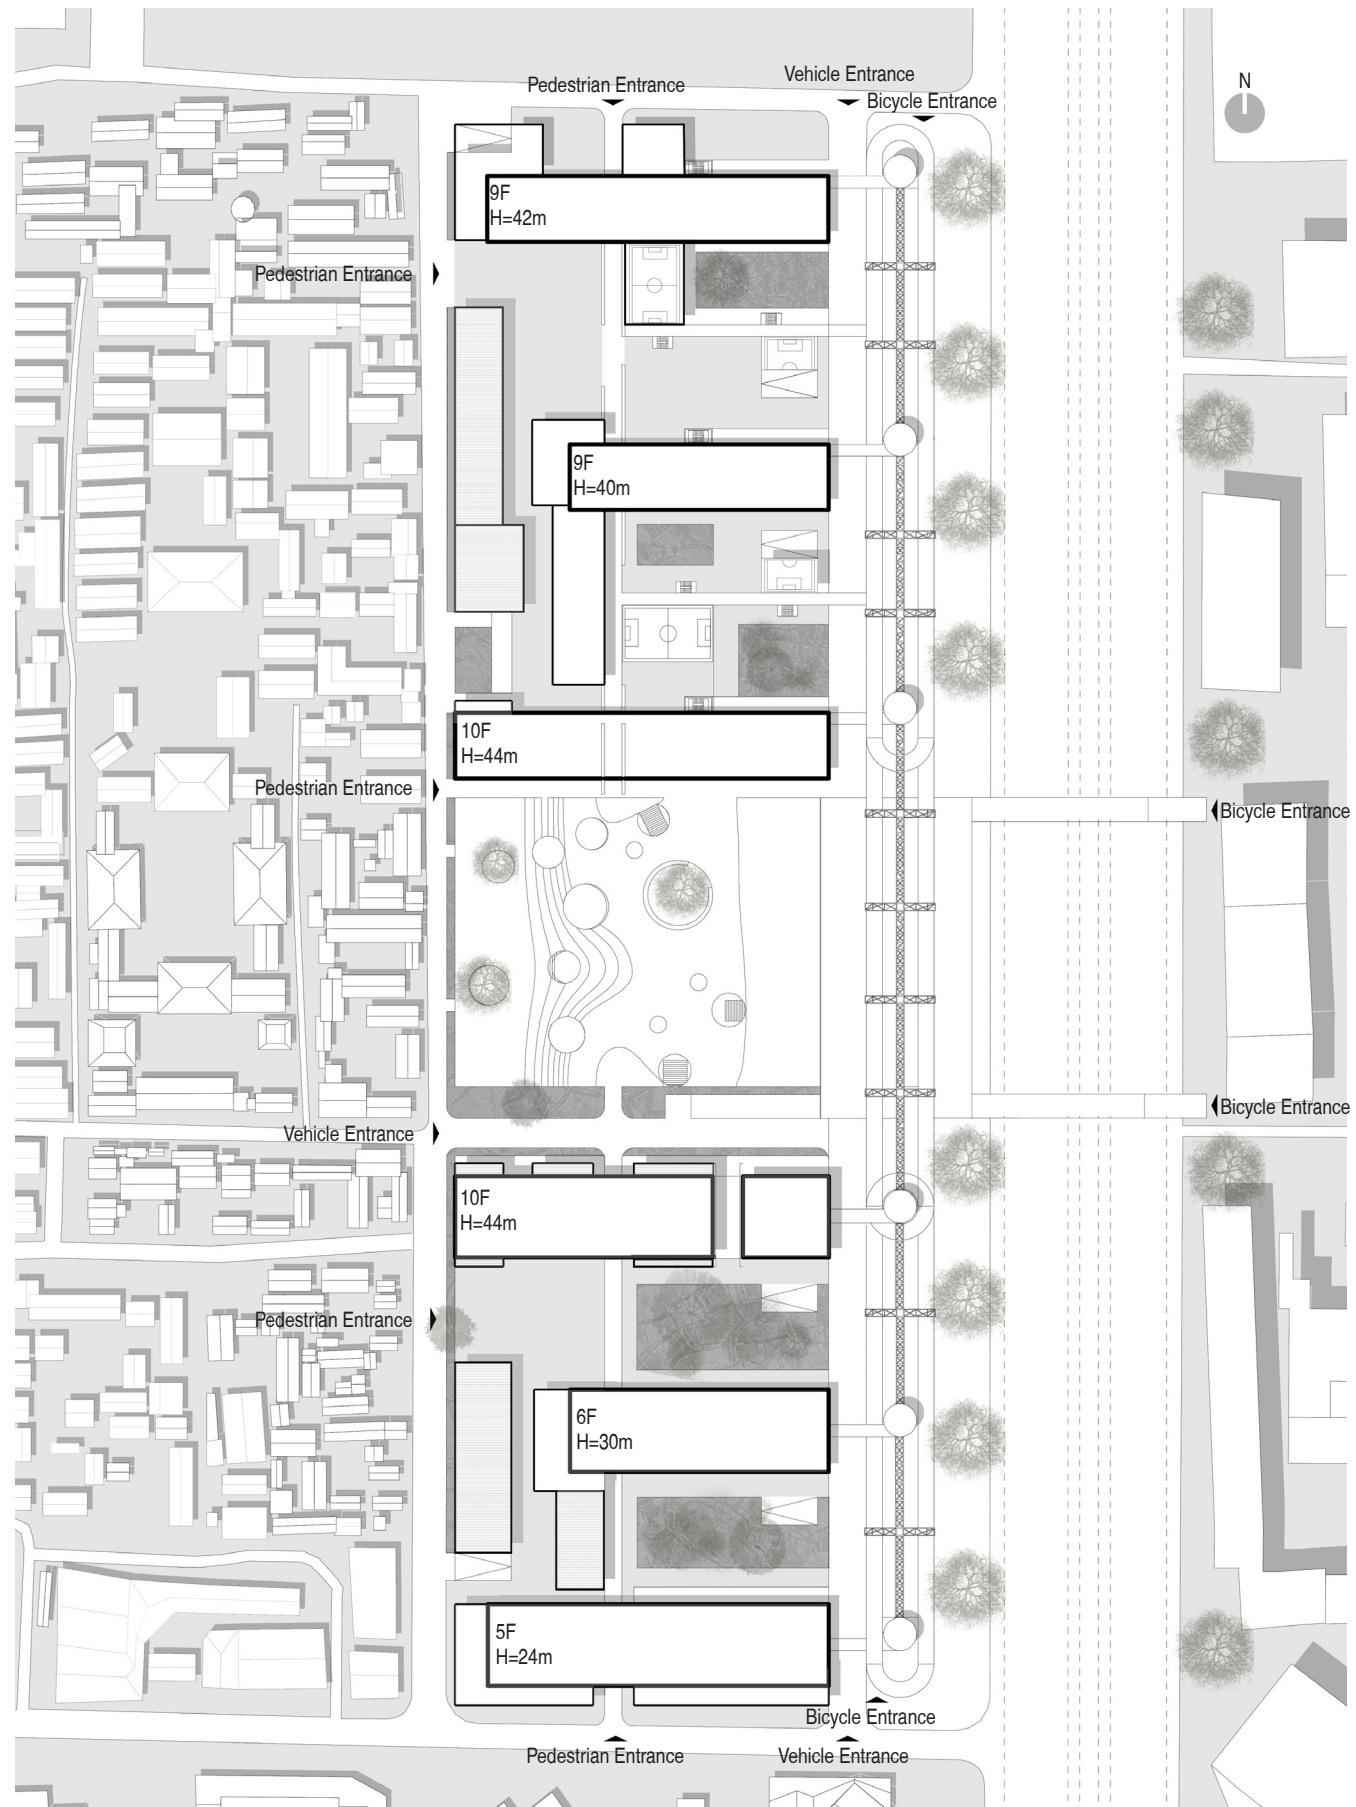


Masterplan



Ground Floor Plan

Typical Block

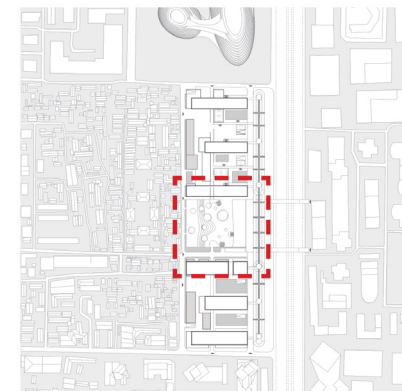

Earth-sheltered Space

In the central area of the entire residential zone, we have designed a large earth-sheltered activity building adjacent to the public road. On the ground level, people can sit casually against the frames to watch movies, and bicycles can ride along the sloped surfaces. Trees emerge from the ground through openings, which also provide natural lighting for the underground public spaces.